



RUA SALUSTIANO BARRETO

66.31

passoio

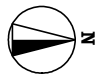

RUA JOAO FERNANDES GAMA

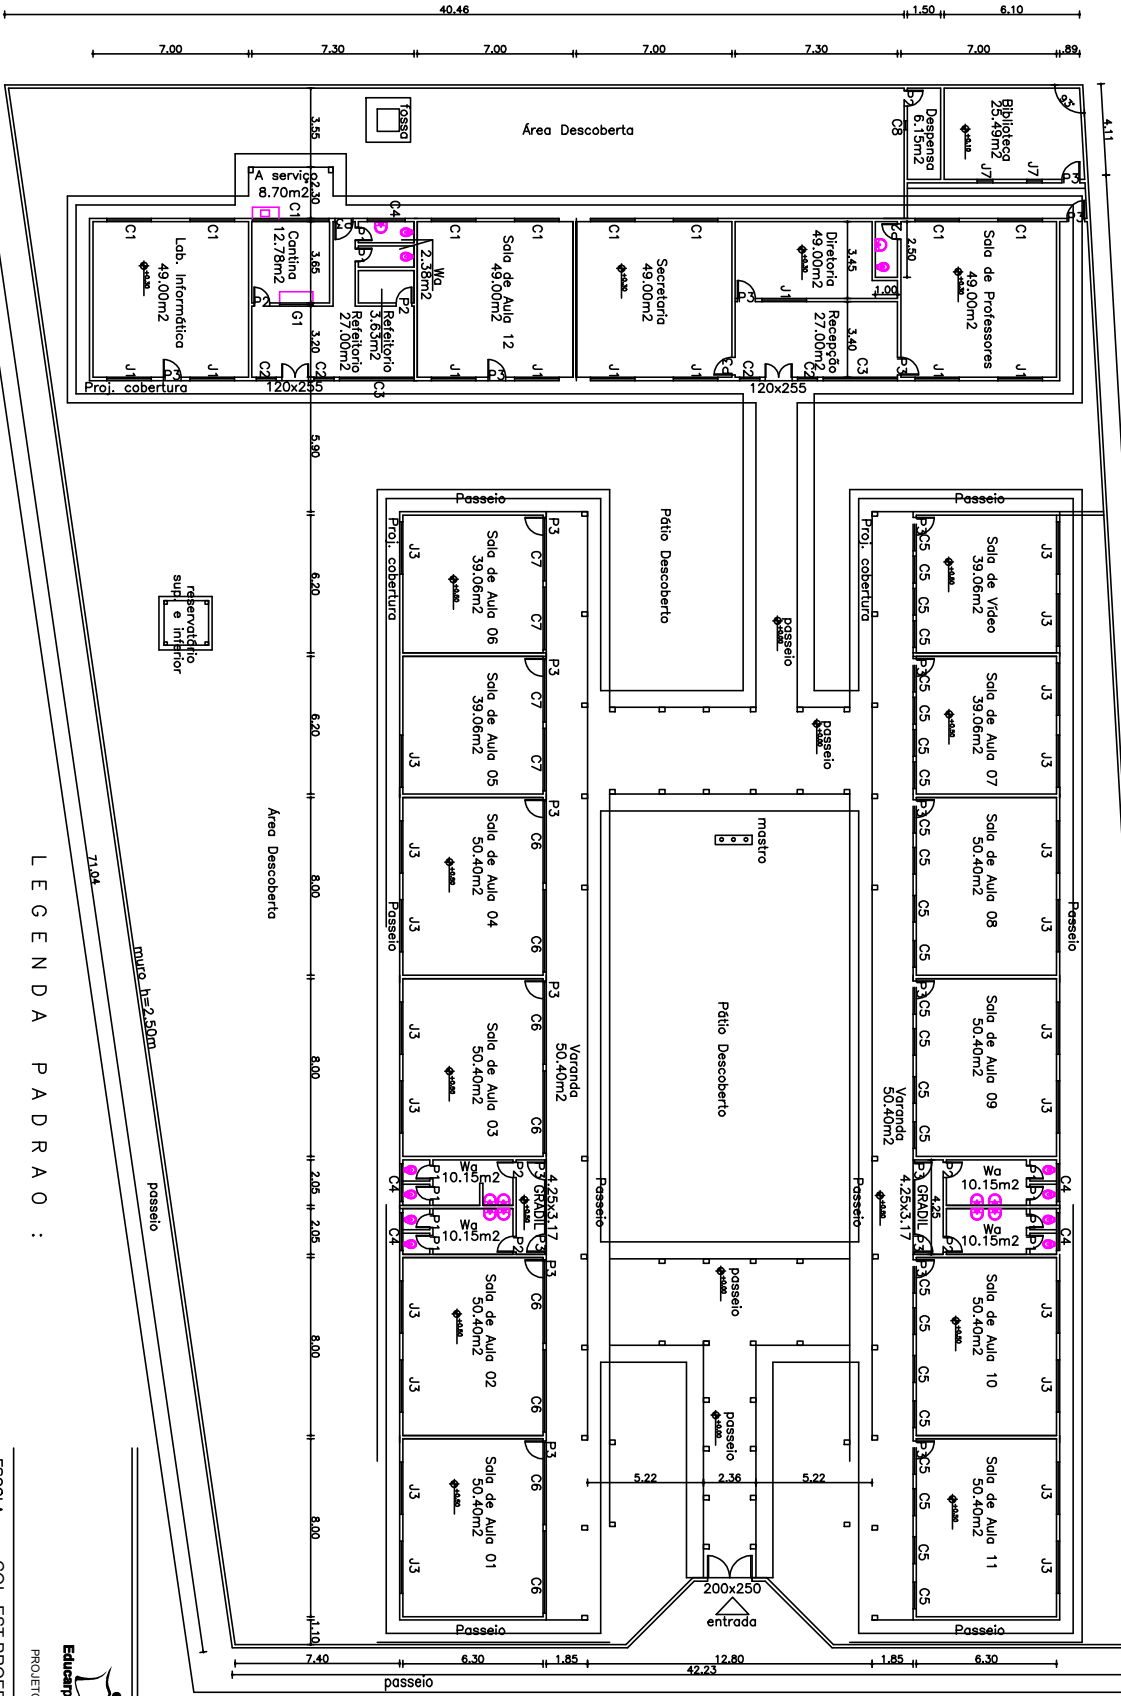

LEGENDA PADRAO :

- Ad - Área Descoberta
- Ar - Arquivo
- Ca - Cozinha
- De - Despensa
- Di - Diretoria
- Dm - Dep. Mt. Limpeza
- Dp - Dep. Mt. Escalar
- Gu - Guardio
- Jd - Jardim
- Pc - Pátio Coberto
- Pd - Pátio Descoberto
- Qd - Quadra
- S - Sala de Aula
- Se - Secretaria
- Sp - Sala de Professores
- Sv - Sala de Vídeo
- Wa - Sanit. de Alunos
- Wf - Sanit. de Funcionários

- LEGENDA:
- J1=2,00 X 1,40 H=1,10
 - J2=3,45 X 0,50 H=2,20
 - J3=2,40 X 1,10 H=1,10
 - J4=0,70 X 1,10 H=1,00
 - C1=2,00 X 1,00 H=1,50
 - C2=0,90 X 1,45 H=1,10
 - C3=3,35 X 1,45 H=1,10
 - C4=1,70 X 0,50 H=2,10
 - C5=1,20 X 0,25 H=2,35
 - C6=3,70 X 0,25 H=2,45
 - C7=2,80 X 0,25 H=2,45
 - C8=0,40 X 0,20 H=2,40
 - G1=1,50 X 1,15 H=0,95
 - P1= 60 x 210
 - P2= 70 x 210
 - P3= 80 x 210

OBS: PETRIL EM MARMORE. NÃO EXISTE SOLARIA



GOVERNO DA BAHIA
Secretaria da Educação
COPET/SUPER
PROJETO DE EDUCAÇÃO DO ESTADO DA BAHIA
AE 7188 - BR

ESCOLA : COL. EST. PROFESSORA SILVA FERREIRA DE BRITO
MUNICÍPIO : RIBEIRA DO POMBAI
ENDEREÇO : RUA JOÃO FERNANDES GAMA, 523, CENTRO

PLANTA BAIXA

GBM Engenharia e Arquitetura

Projeto : 03/03

Arquiteto : 29133955-PR/DWG

Desenho : GBM

Revisão : GBM

Data : FEVEREIRO/2005

Escala : 1:250

Arquiteto : 29133955-PR/DWG